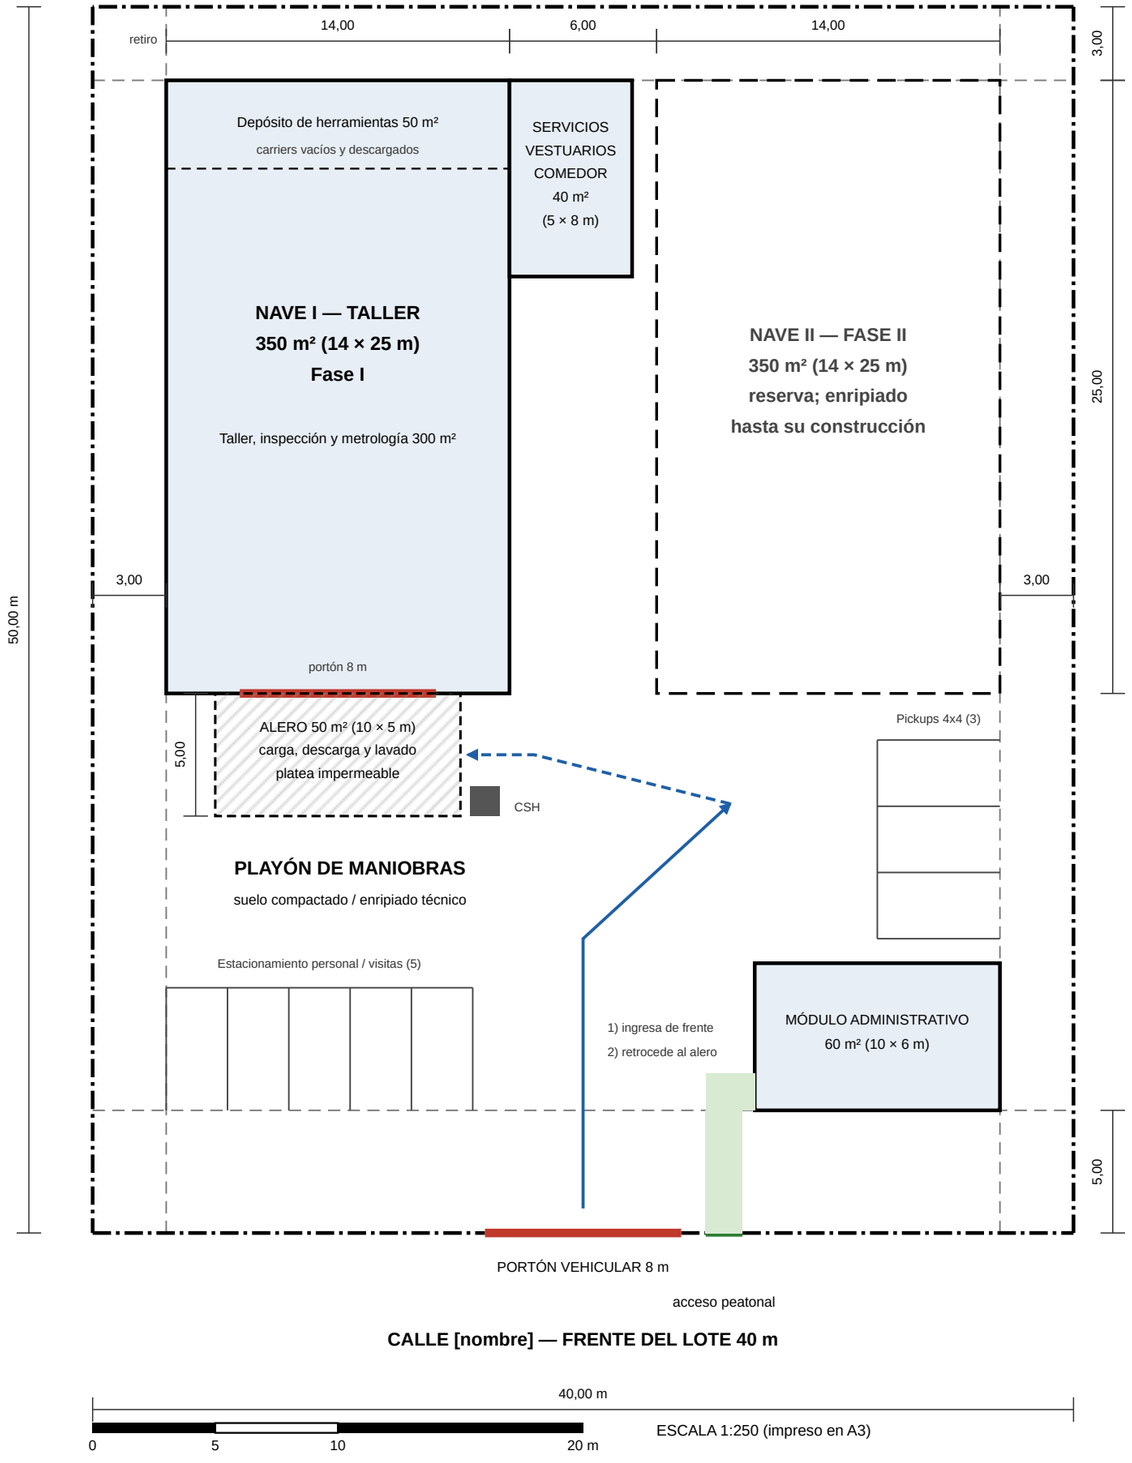


REFERENCIAS

- Edificación Fase I (cubierta)
- Semicubierto (alero)
- Fase II (futura)
- Cerco perimetral olímpico (≈172 m)
- Línea de retiro (supuesta: frente 5 m, laterales y fondo 3 m)
- Portón vehicular
- Recorrido camión rígido ≤10 m (punteado: marcha atrás)
- CSH: cámara separadora de hidrocarburos

CUADRO DE SUPERFICIES

Lote (40 × 50 m)	2.000 m²
Nave I — taller 300 m² + depósito 50 m²	350 m²
Módulo administrativo	60 m²
Servicios / vestuarios / comedor	40 m²
Cubierta Fase I	**450 m²**
Semicubierta (alero)	50 m²
Total a construir Fase I	**500 m²**
Playón y estacionamientos Fase I (incl. reserva)	≈ 970 m²
Nave II — Fase II	350 m²
FOS Fase I / con Fase II	25 % / 42,5 %

NOTAS

1. Vehículo de diseño: pickups y camión rígido con hidrogrúa de hasta 10 m. Los semirremolques no ingresan al predio.
2. En el predio no se almacenan ni manipulan materiales energéticos ni fuentes radiactivas.
3. Retiros, FOS y alturas a verificar con el reglamento del Parque Industrial Capital.
4. Orientación (Norte) y nombre de la calle según plano de mensura del lote adjudicado.
5. Nave I: altura libre 7 m o más, estructura apta para monorriel de 3 a 5 t (Fase II); piso H30.
6. Lavado bajo alero con platea impermeable y CSH.
7. Cotas en metros.

ANTEPROYECTO — NO APTO PARA CONSTRUCCIÓN

PROYECTO

Base operativa, taller de inspección y metrología y depósito de herramientas de pozo

PROPIETARIO / PROPONENTE

XANTRAX S.R.L. — CUIT 30-71457180-6

UBICACIÓN

Parque Industrial Capital, Neuquén — Lote N° [____], Manzana [____]

PLANO

Implantación general — Fase I y reserva Fase II

ESCALA 1:250 — HOJA A3 — LÁMINA 1 de 1

Revisión: A — Fecha: [____]

Esquema base para desarrollo en CAD.

PROFESIONAL RESPONSABLE

Nombre: _____

Matrícula N°: _____

Firma: _____